PLANIMETRIA I.T.I.S. "P.PALEOCAPA"

Aggiornato a: Settembre 2025

SEGNALETICA DI SICUREZZA

PUNTI DI RACCOLTA

1 3 5
2 4 6

- IDRANTE
- IDRANTE SOPRASUOLO
- ESTINTORE
- LANCIA ANTINCENDIO
- USCITA DI EMERGENZA A DX
- USCITA DI EMERGENZA A SIN.
- SGANCIO ENERGIA ELETTR.
- QUADRO ELETTRICO
- SCALA DISC. A SIN.
- SCALA DISC. A DX
- SCALA ASCEND. A DX
- SCALA ASCEND. A SIN
- LOCALE INFERMERIA
- CASSETTA DI MEDICAZIONE
- SPAZIO CALMO

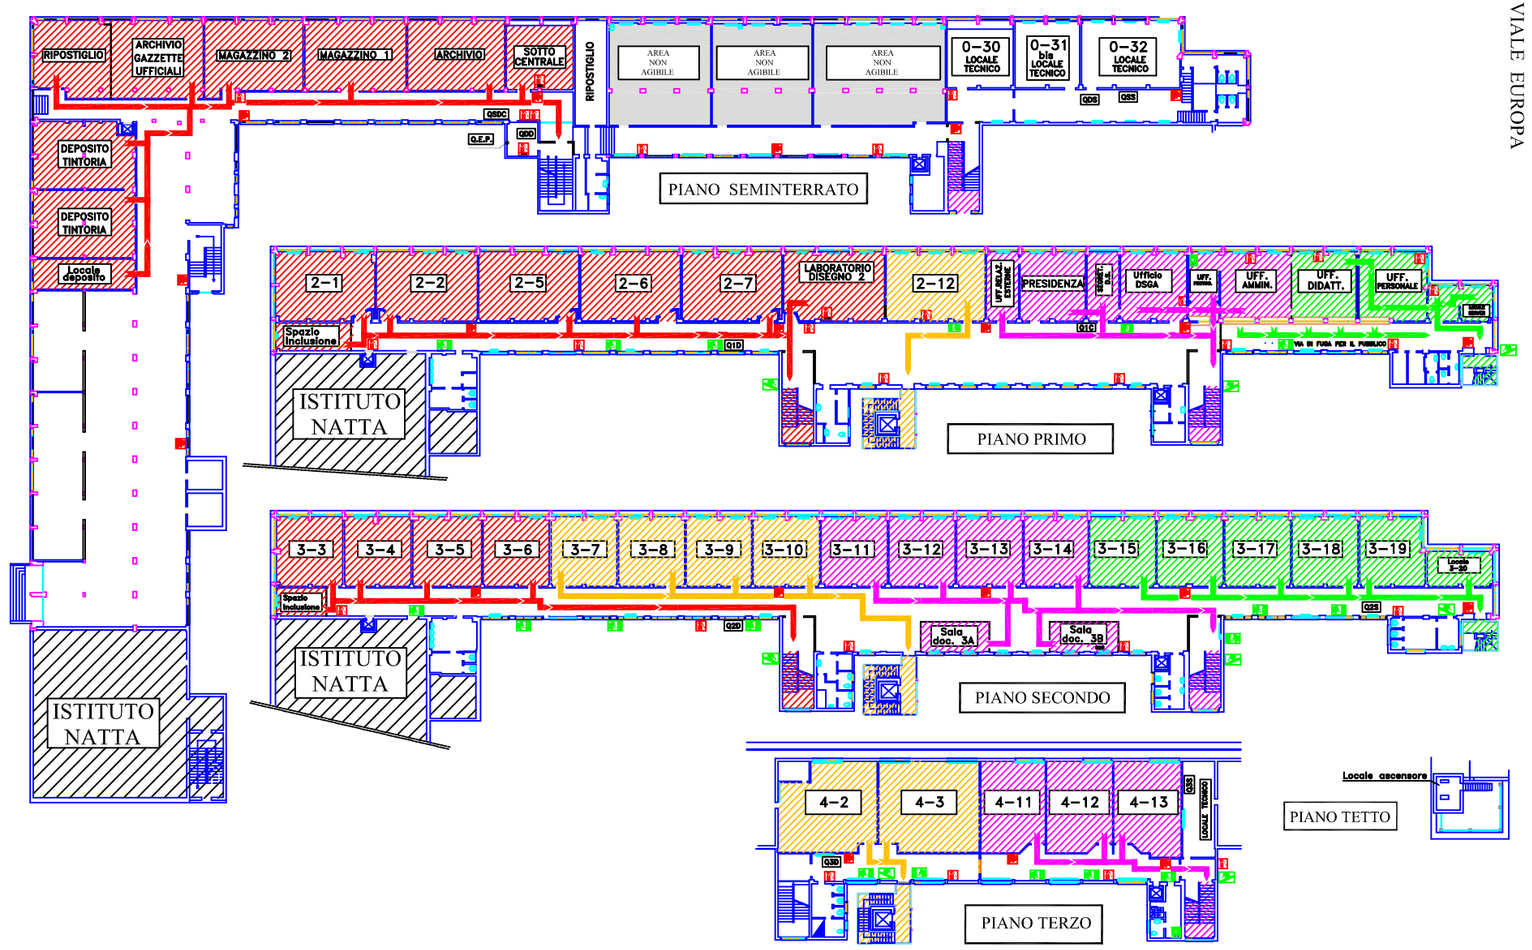

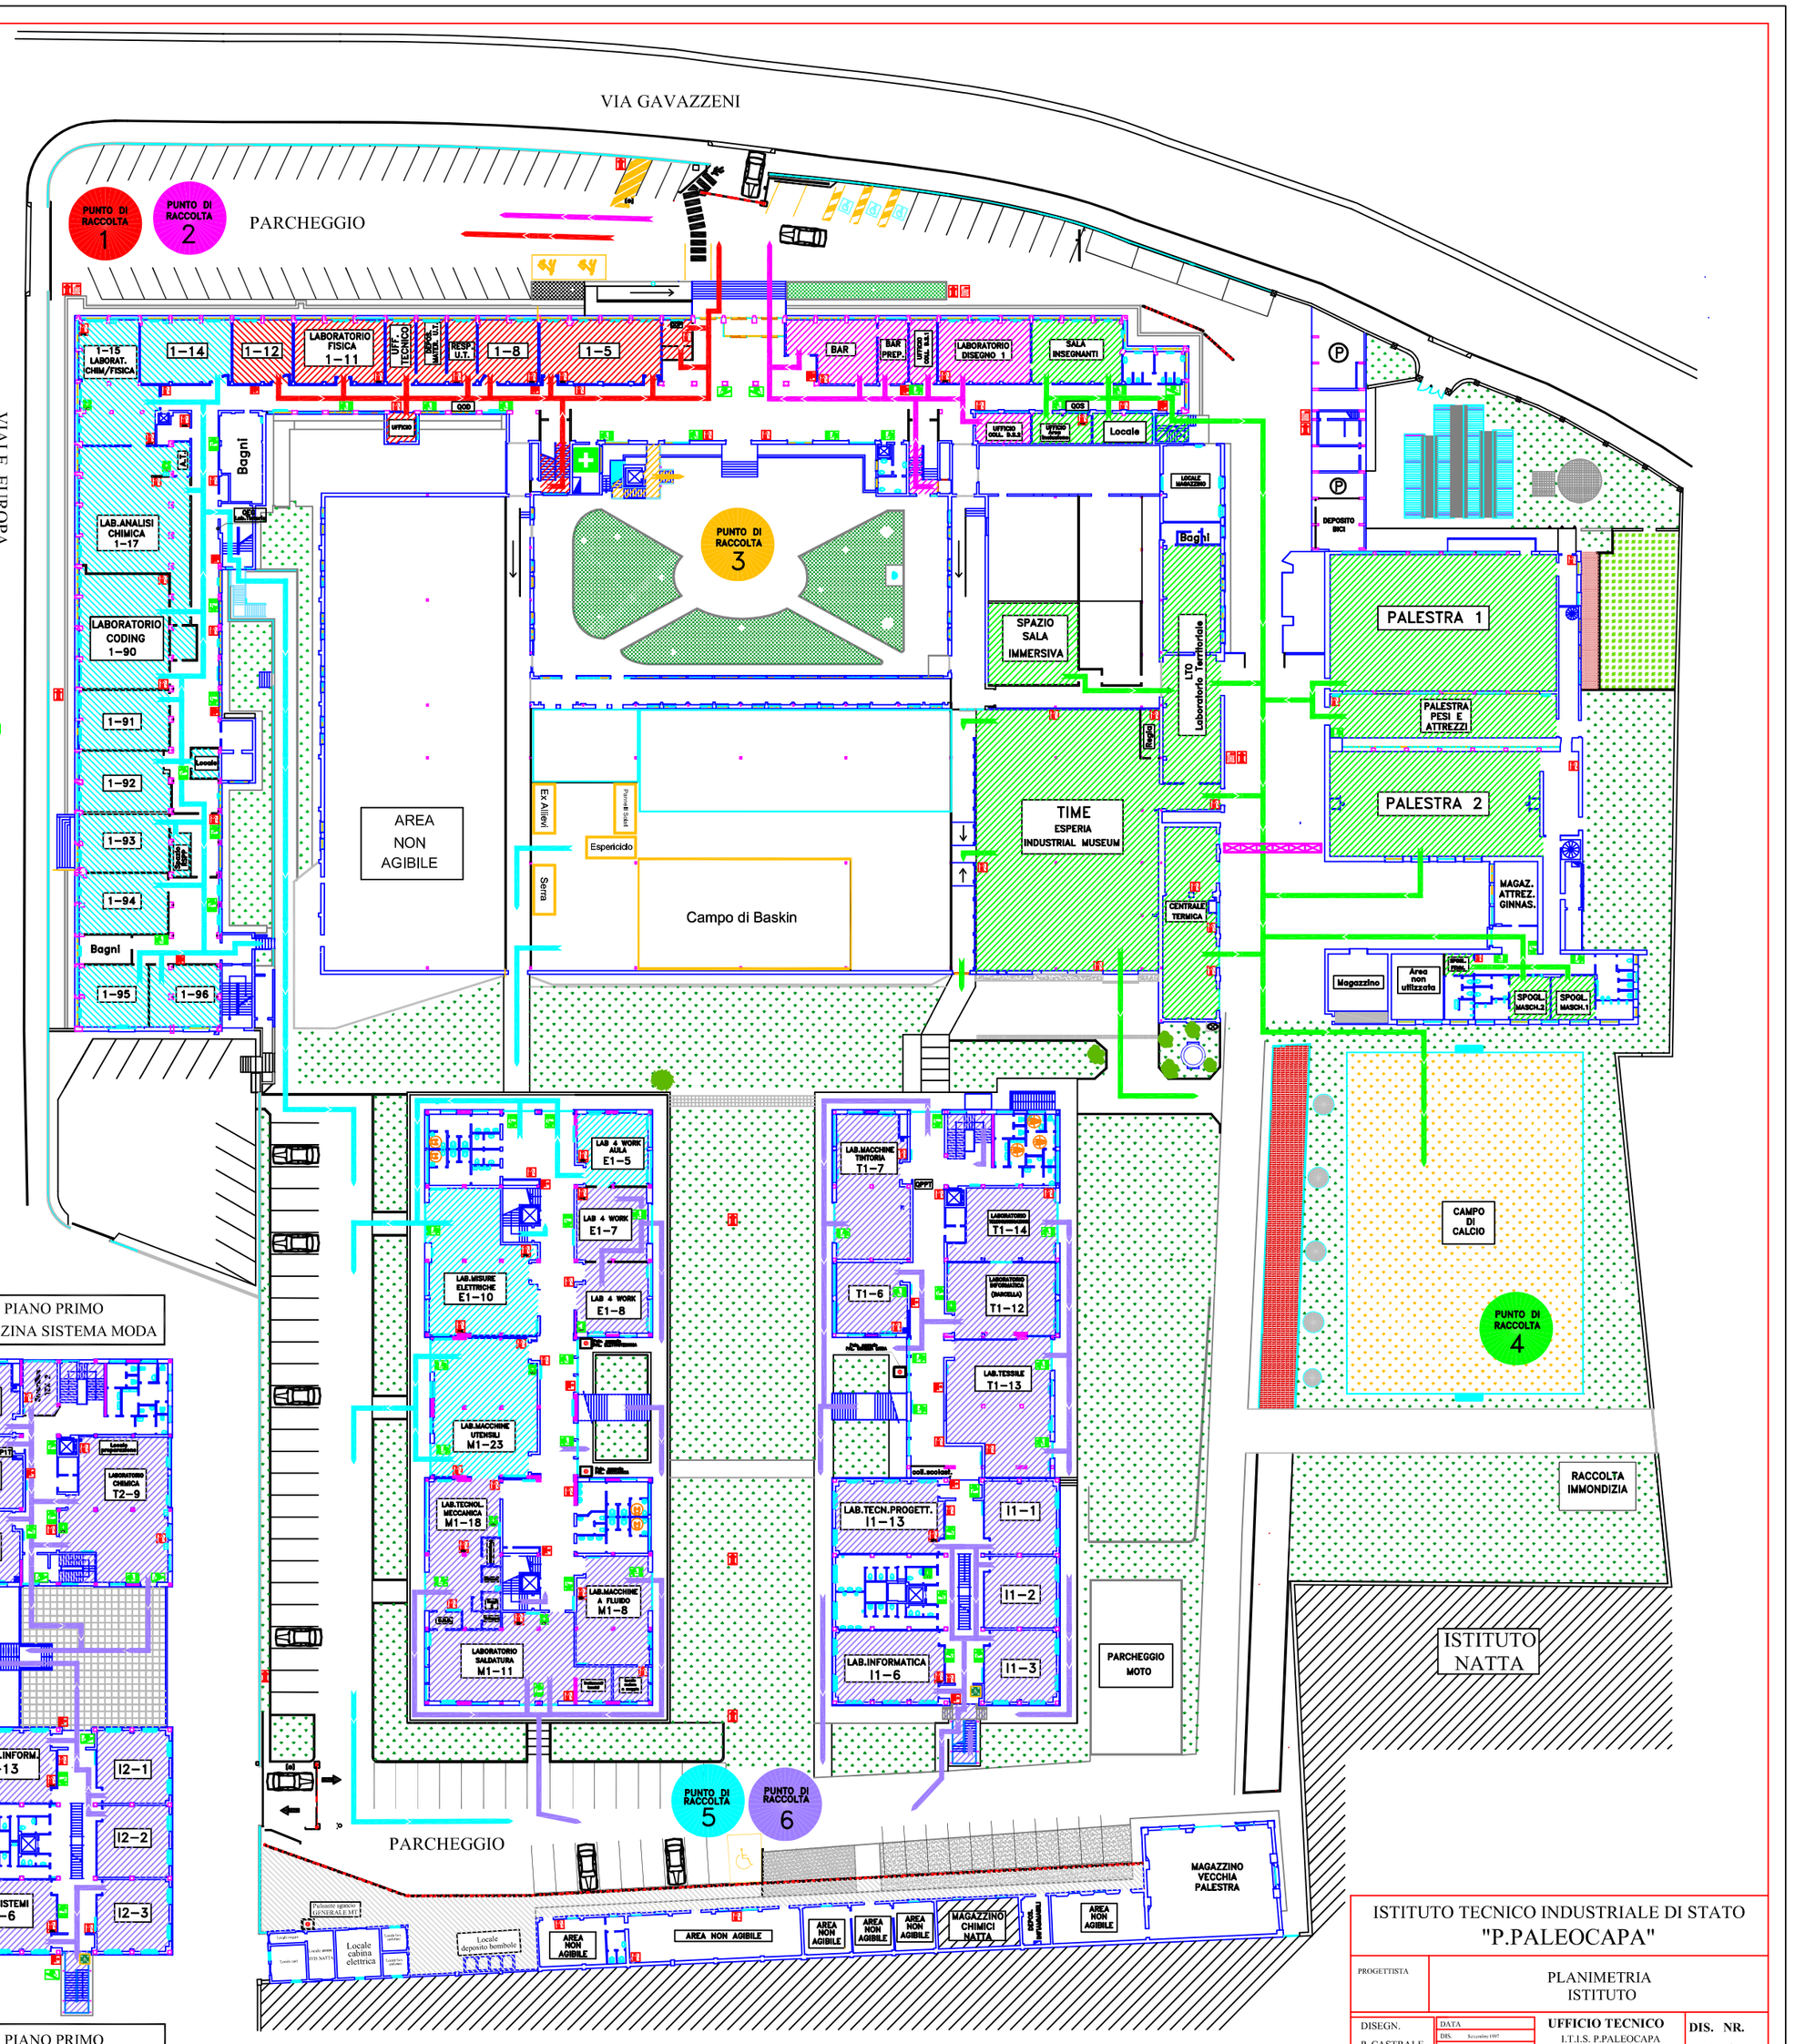

PIANO SECONDO PALAZZINA ELETTROTECNICA

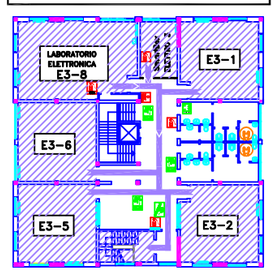

PIANO PRIMO PALAZZINA ELETTROTECNICA

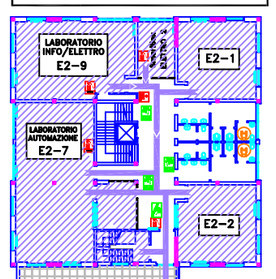

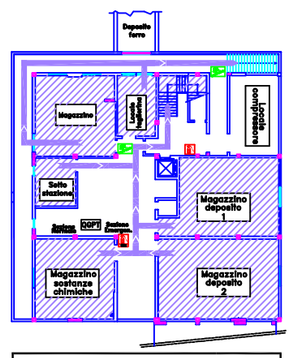

PALAZZINA SISTEMA MODA PIANO SEMINTERRATO

PIANO SECONDO PALAZZINA SISTEMA MODA

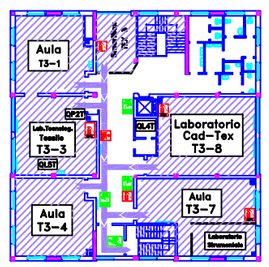

PIANO PRIMO PALAZZINA SISTEMA MODA

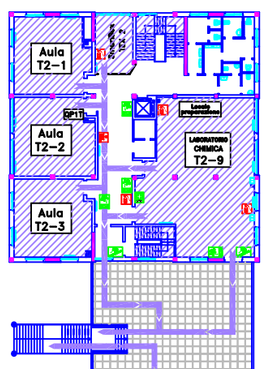

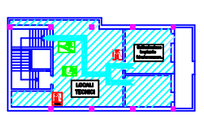

PALAZZINA ELETTROTECNICA PIANO SEMINTERRATO

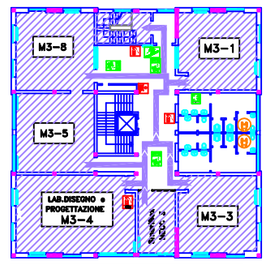

PIANO SECONDO PALAZZINA MECCANICA

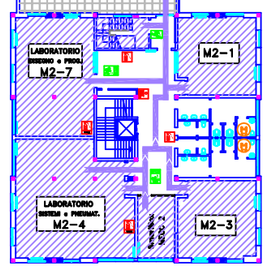

PIANO PRIMO PALAZZINA MECCANICA

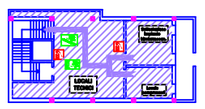

PIANO SEMINTERRATO PALAZZINA MECCANICA

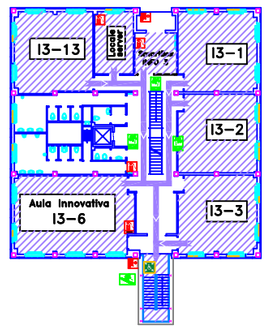

PIANO SECONDO PALAZZINA INFORMATICA

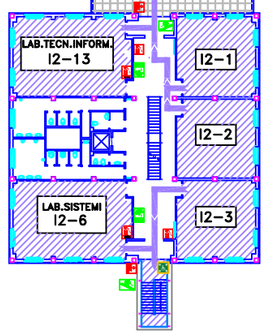

PIANO PRIMO PALAZZINA INFORMATICA

ISTITUTO TECNICO INDUSTRIALE DI STATO
"P.PALEOCAPA"

PROGETTISTA	PLANIMETRIA ISTITUTO		
DISEGN. P. CASTRALE S. FERRARI	DATA Dicembre 1997	UFFICIO TECNICO I.T.I.S. P.PALEOCAPA Via Gavazzeni n° 29 24125 BERGAMO	DIS. NR. 1/s
	VISTO		
	SCALA Adottato		
ins. ed.: esper.....dwg	MODIFICHE		